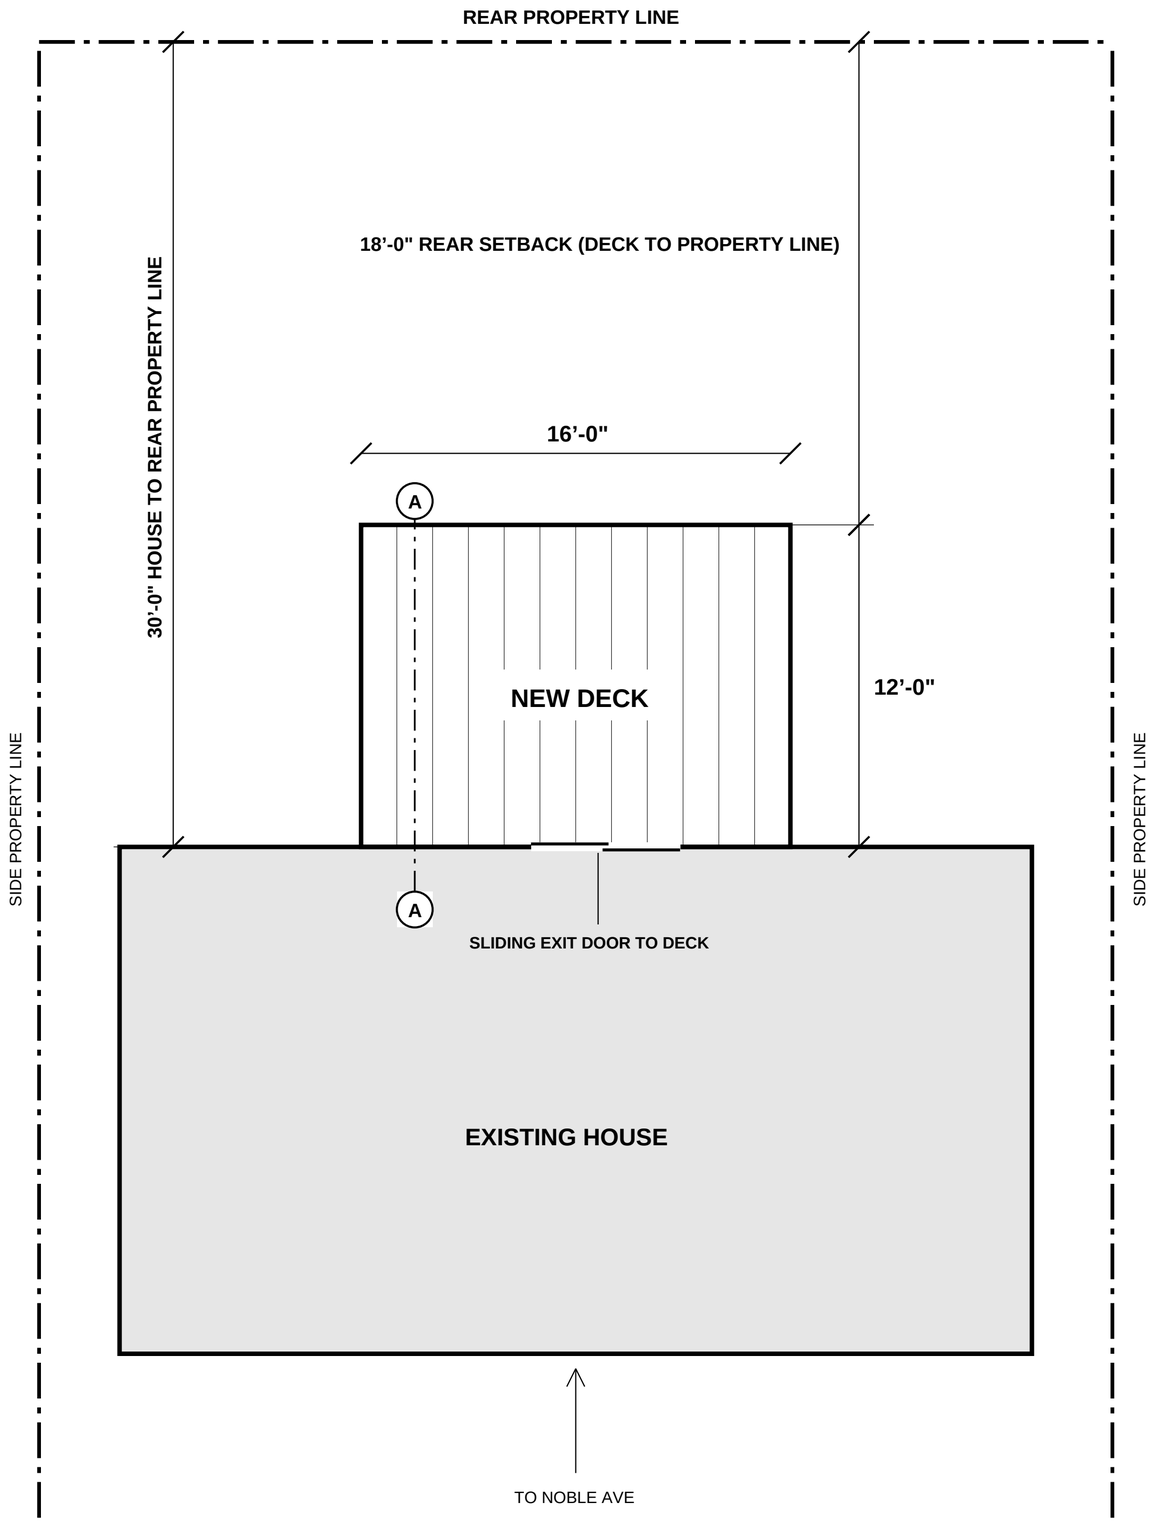

SITE PLAN

SCALE 1/4 IN = 1 FT

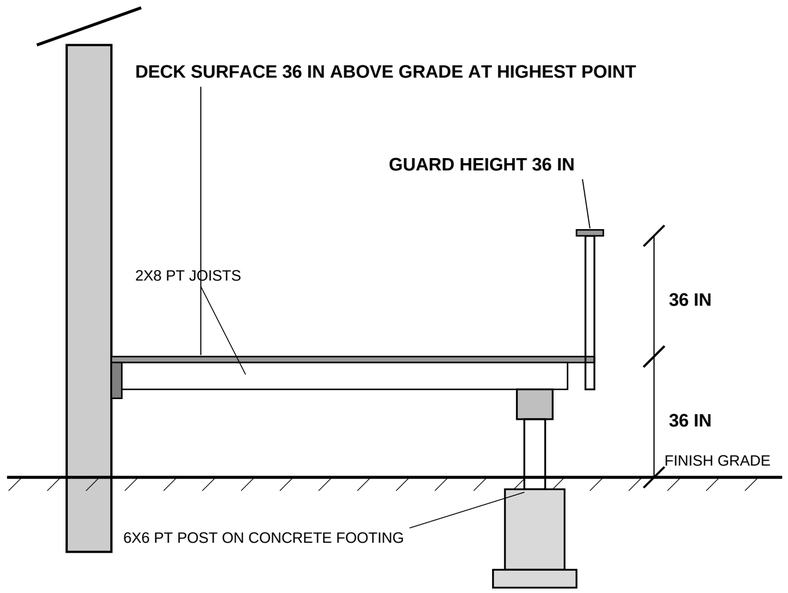

SECTION A-A

NOT TO SCALE

FRAMING NOTES

1. ATTACHED TO REAR WALL OF HOUSE
2. LEDGER: 2X10 PT, 1/2 IN THROUGH-BOLTS AT 16 IN O.C. INTO RIM JOIST
3. JOISTS: 2X8 PT AT 16 IN O.C. WITH HANGERS AT LEDGER
4. BEAM: (2) 2X10 PT ON 6X6 PT POSTS
5. FOOTINGS: CONCRETE, 18 IN DIA. BY 24 IN DEEP
6. DECKING: 5/4 X 6 PT BOARDS WITH 1/8 IN GAP
7. HARDWARE: HOT-DIPPED GALVANIZED OR STAINLESS STEEL
8. DECK SERVES AS LANDING AT SLIDING EXIT DOOR
9. CONTRACTOR TO VERIFY ALL DIMENSIONS IN FIELD

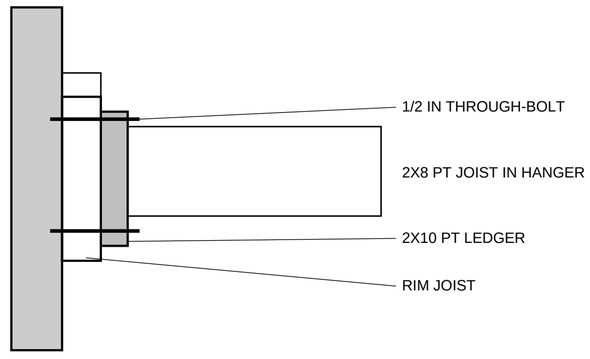

LEDGER DETAIL

NOT TO SCALE

PREPARED BY

Sample Drafting Studio
100 Example Way
Campbell, CA 95008

DECK ADDITION

Project site
14630 Noble Ave, San Jose, CA 95132

APN
595-31-001

Zoning
R-1-8

Owner
Homeowner of record

Date
10/31/2026

Scale
1/4 in = 1 ft

REVISIONS

SAMPLE FOR DEMO
Not a real project

Sheet

A-1